


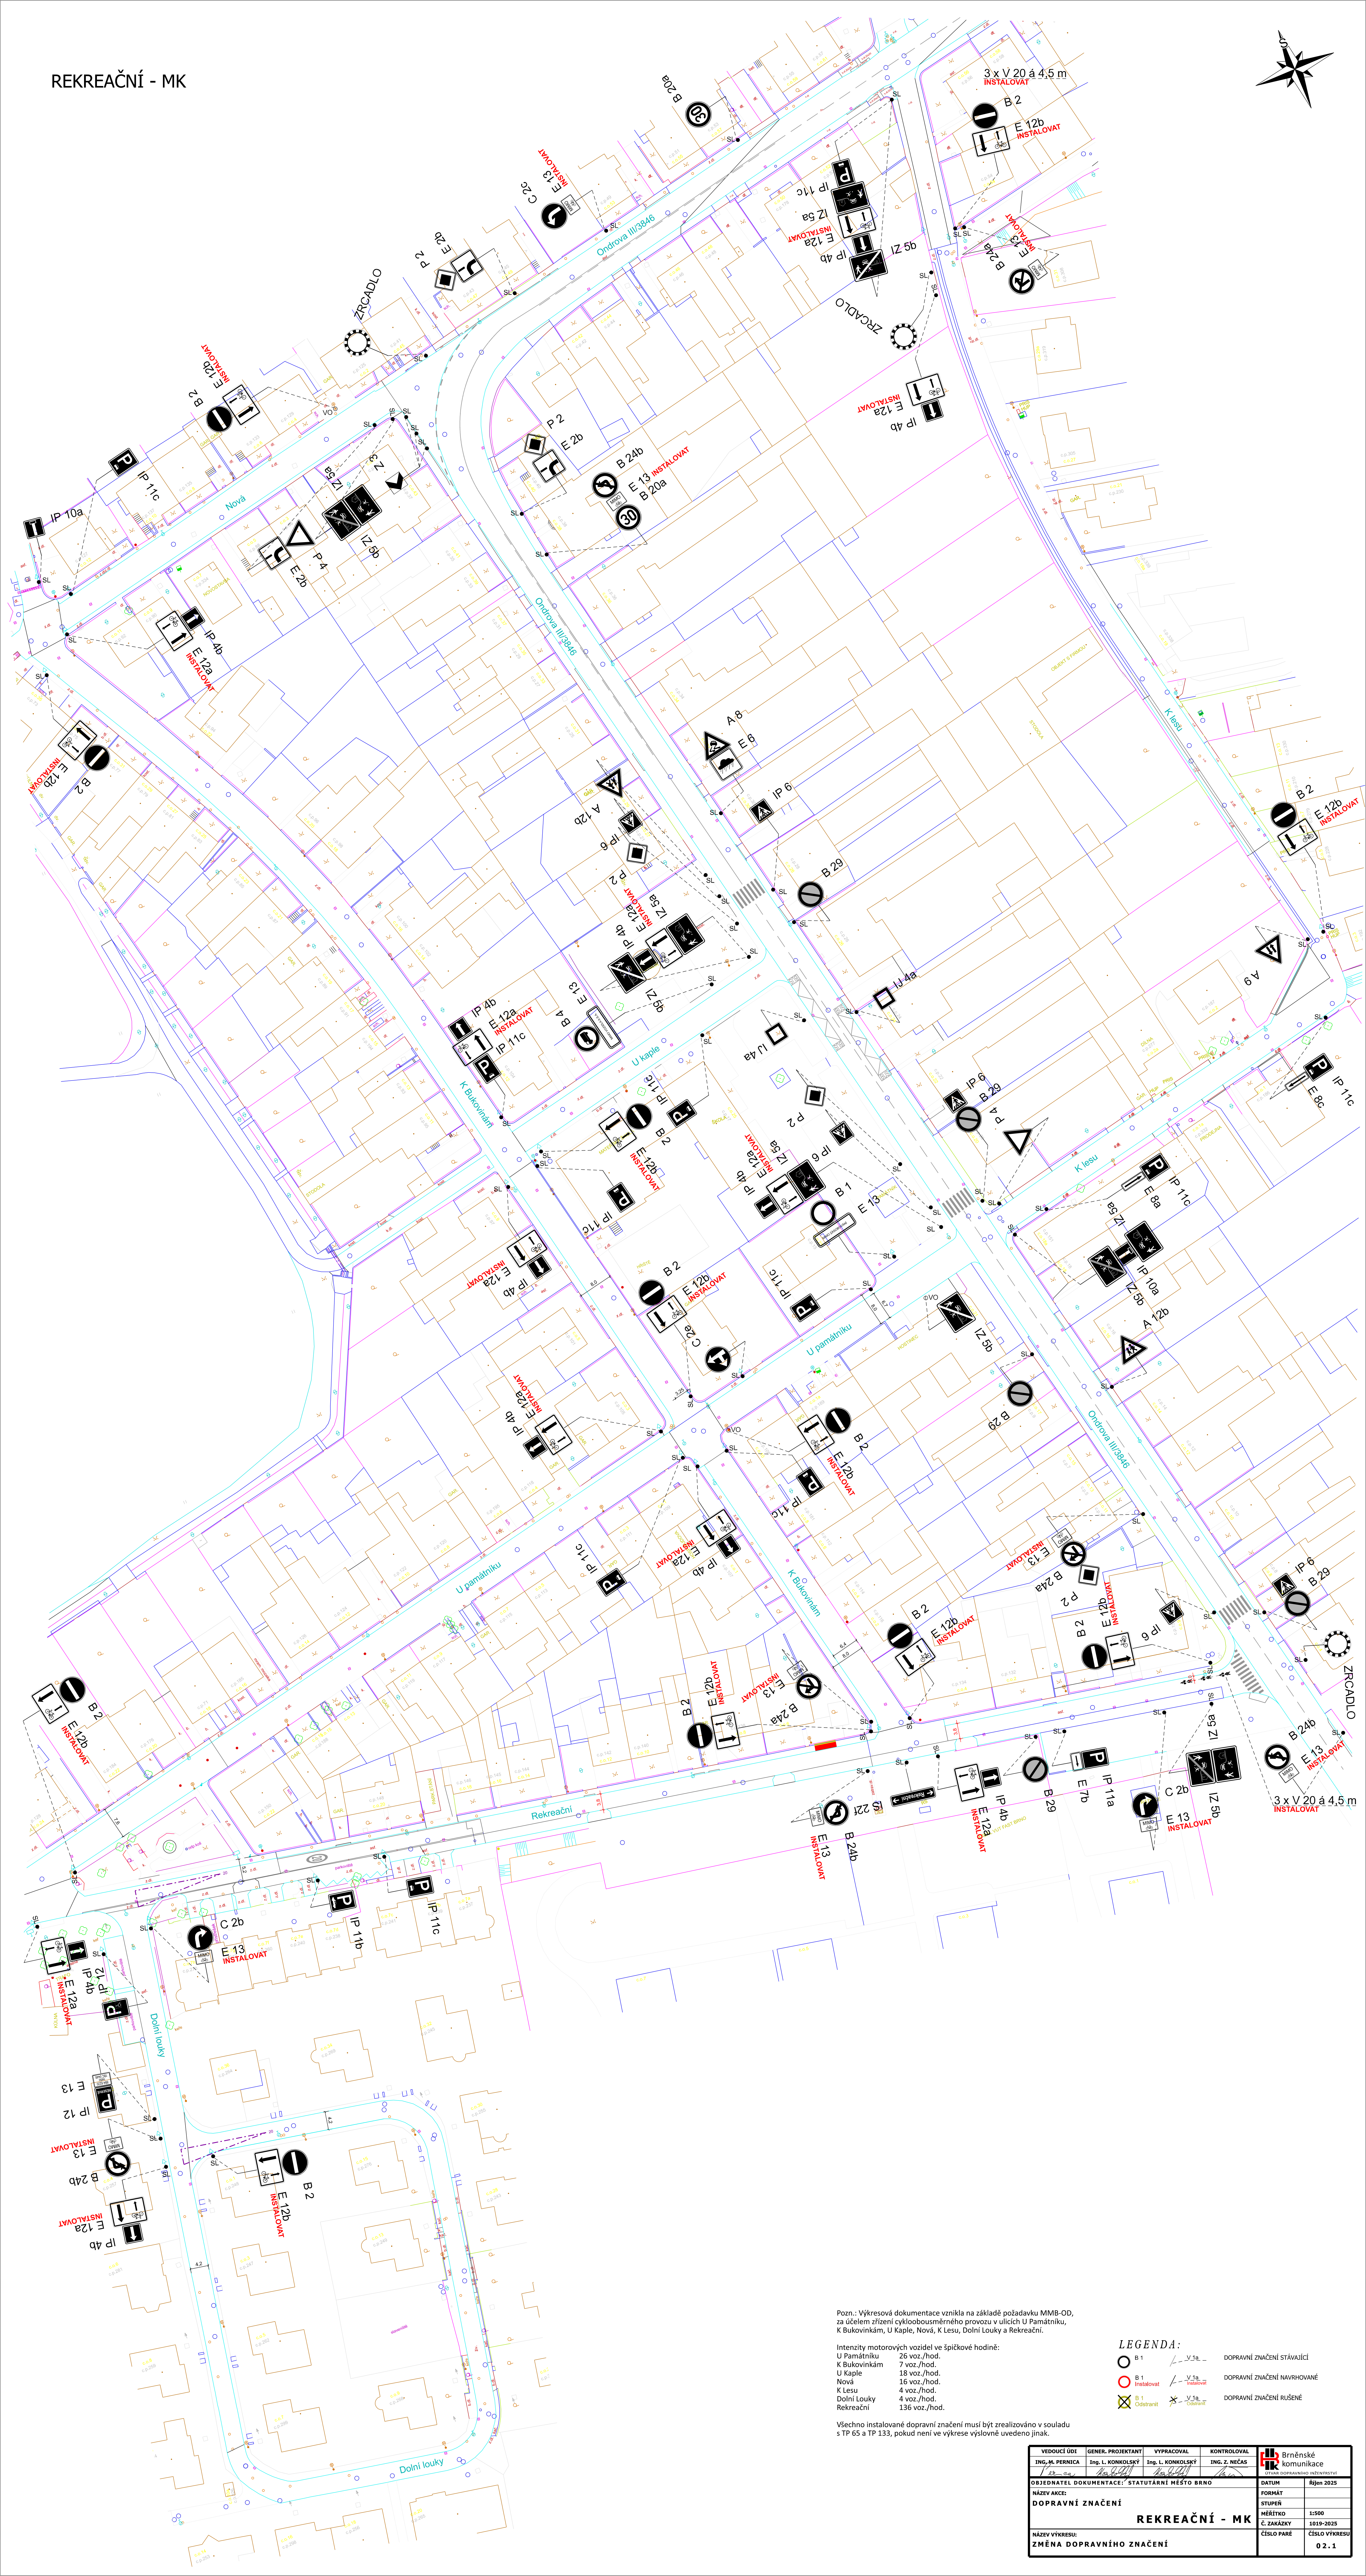

Všechno instalované dopravní značení musí být zrealizováno v souladu s TP 65 a TP 133, pokud není ve výkrese výslovně uvedeno jinak.

 B 1	 - V 1a -	DOPRAVNÍ ZNAČENÍ STÁVAJÍCÍ
 B 1 Instalovat	 - V 1a - Instalovat	DOPRAVNÍ ZNAČENÍ NAVRHOVANÉ
B 1 Odstranit	- V 1a - Odstranit	DOPRAVNÍ ZNAČENÍ RUŠENÉ

YEDOUČÍ ÚDÍ	GENÉR. PROJEKTANT	VÝPRAVČÁK	KONTROLOVÁTEL	 Brněnské komunikační a projektové služby, s.r.o. BRNO, PRAHA, OSTRAVA, PRAHA
ING. M. PERINCA	ING. L. KONKOLSKÝ	ING. L. KONKOLSKÝ	ING. Z. NEČAS	
OJEDNATELNÍ DOKUMENTACE - STATUTÁRNÍ MĚSTO BRNO NÁZEY AKCE: DOPRAVNÍ ZNAČENÍ				DATUM Říjen 2025
REKREAČNÍ - MK				FORMÁT A4
				STUPEŇ MĚŘITKO 1:500
NÁZEY VÝHRESDU: ZMĚNA DOPRAVNÍHO ZNAČENÍ				Č. ZÁKAZKY 1019-2025
				ČÍSLO VÝHRESDU 0.2.1