


KOORDINAČNÍ SITUACE
M 1:250

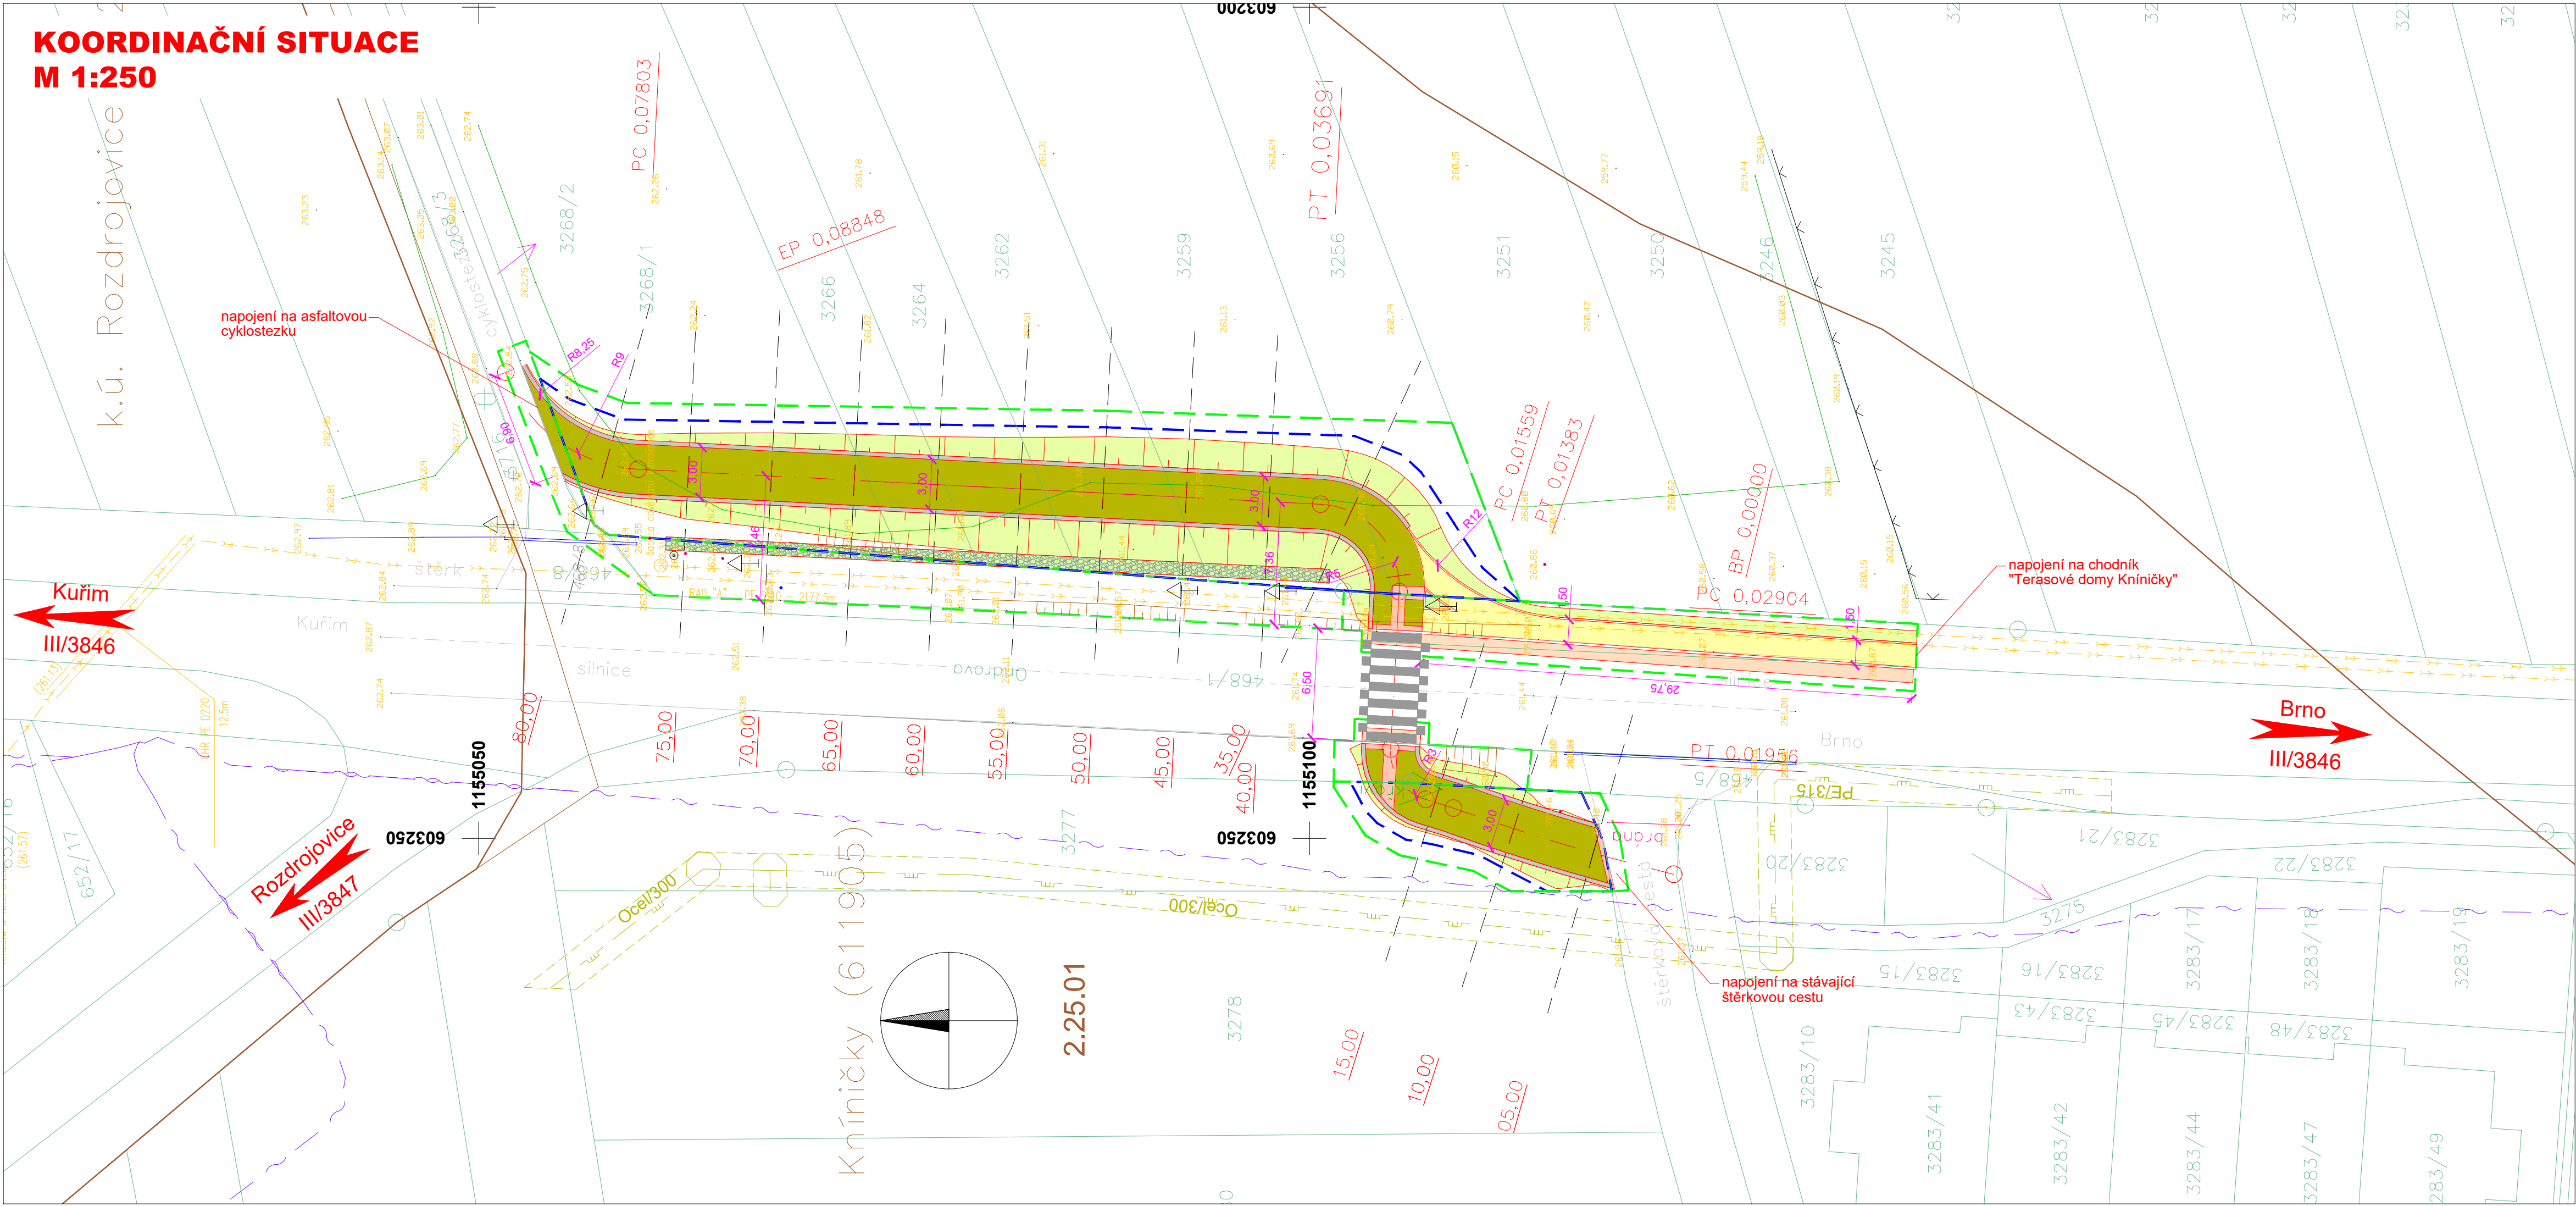

Legenda barev

- stezka - asfalt
- nezpevněná krajnice
- zámková dlažba pro osoby se s níženou schopností pohybu
- chodník - zámková dlažba
- násyp
- oprava komunikace - frézování
- vsakovací rýha

Legenda inženýrských sítí

- Stávající inženýrské sítě:
- datové kabely podzemní
 - plynovod STL
 - splašková kanalizace

Legenda KN

- hranice parcel
- hranice katastrálního území
- hranice BPEJ

Legenda záboru

- trvalý zábor
- dočasný zábor do 1 roku

C

STEZKA PŘI UL. ONDROVA

UMÍSTĚNÍ: BRNO, JIHMORAVSKÝ KRAJ				
OBJEDNATEL: BRNĚNSKÉ KOMUNIKACE a.s., RENNESKÁ TRÍDA 787/1a, 639 00 BRNO - ŠTÝŘICE				
VYPRACOVAL: 	TECH.KONTROLA: 	ZODP.PROJEKTANT: 	MĚŘÍTKO	1 : 250
Martin LUKŠ	Martin LUKŠ	Martin LUKŠ	FORMÁT	4 A4
PROJEKTANT: STAVONA Tender, spol. s r.o.				
E-KONTAKT: WWW.STAVONATENDER.CZ				
STUPEŇ PD: PROJEKTOVÁ DOKUMENTACE PRO VYDÁNÍ SPOLEČNÉHO POVOLENÍ (DUSP)				
ZAKÁZKA: 26/03/2024				
DATUM: KVĚTEN 2024				
C - SITUAČNÍ VÝKRESY			Č.VÝKRESU:	
NÁZEV VÝKRESU: Koordinační situace			KOPIE:	
			C.3	