


VZOROVÝ PŘÍČNÝ ŘEZ ULIČNÍM PROSTOREM

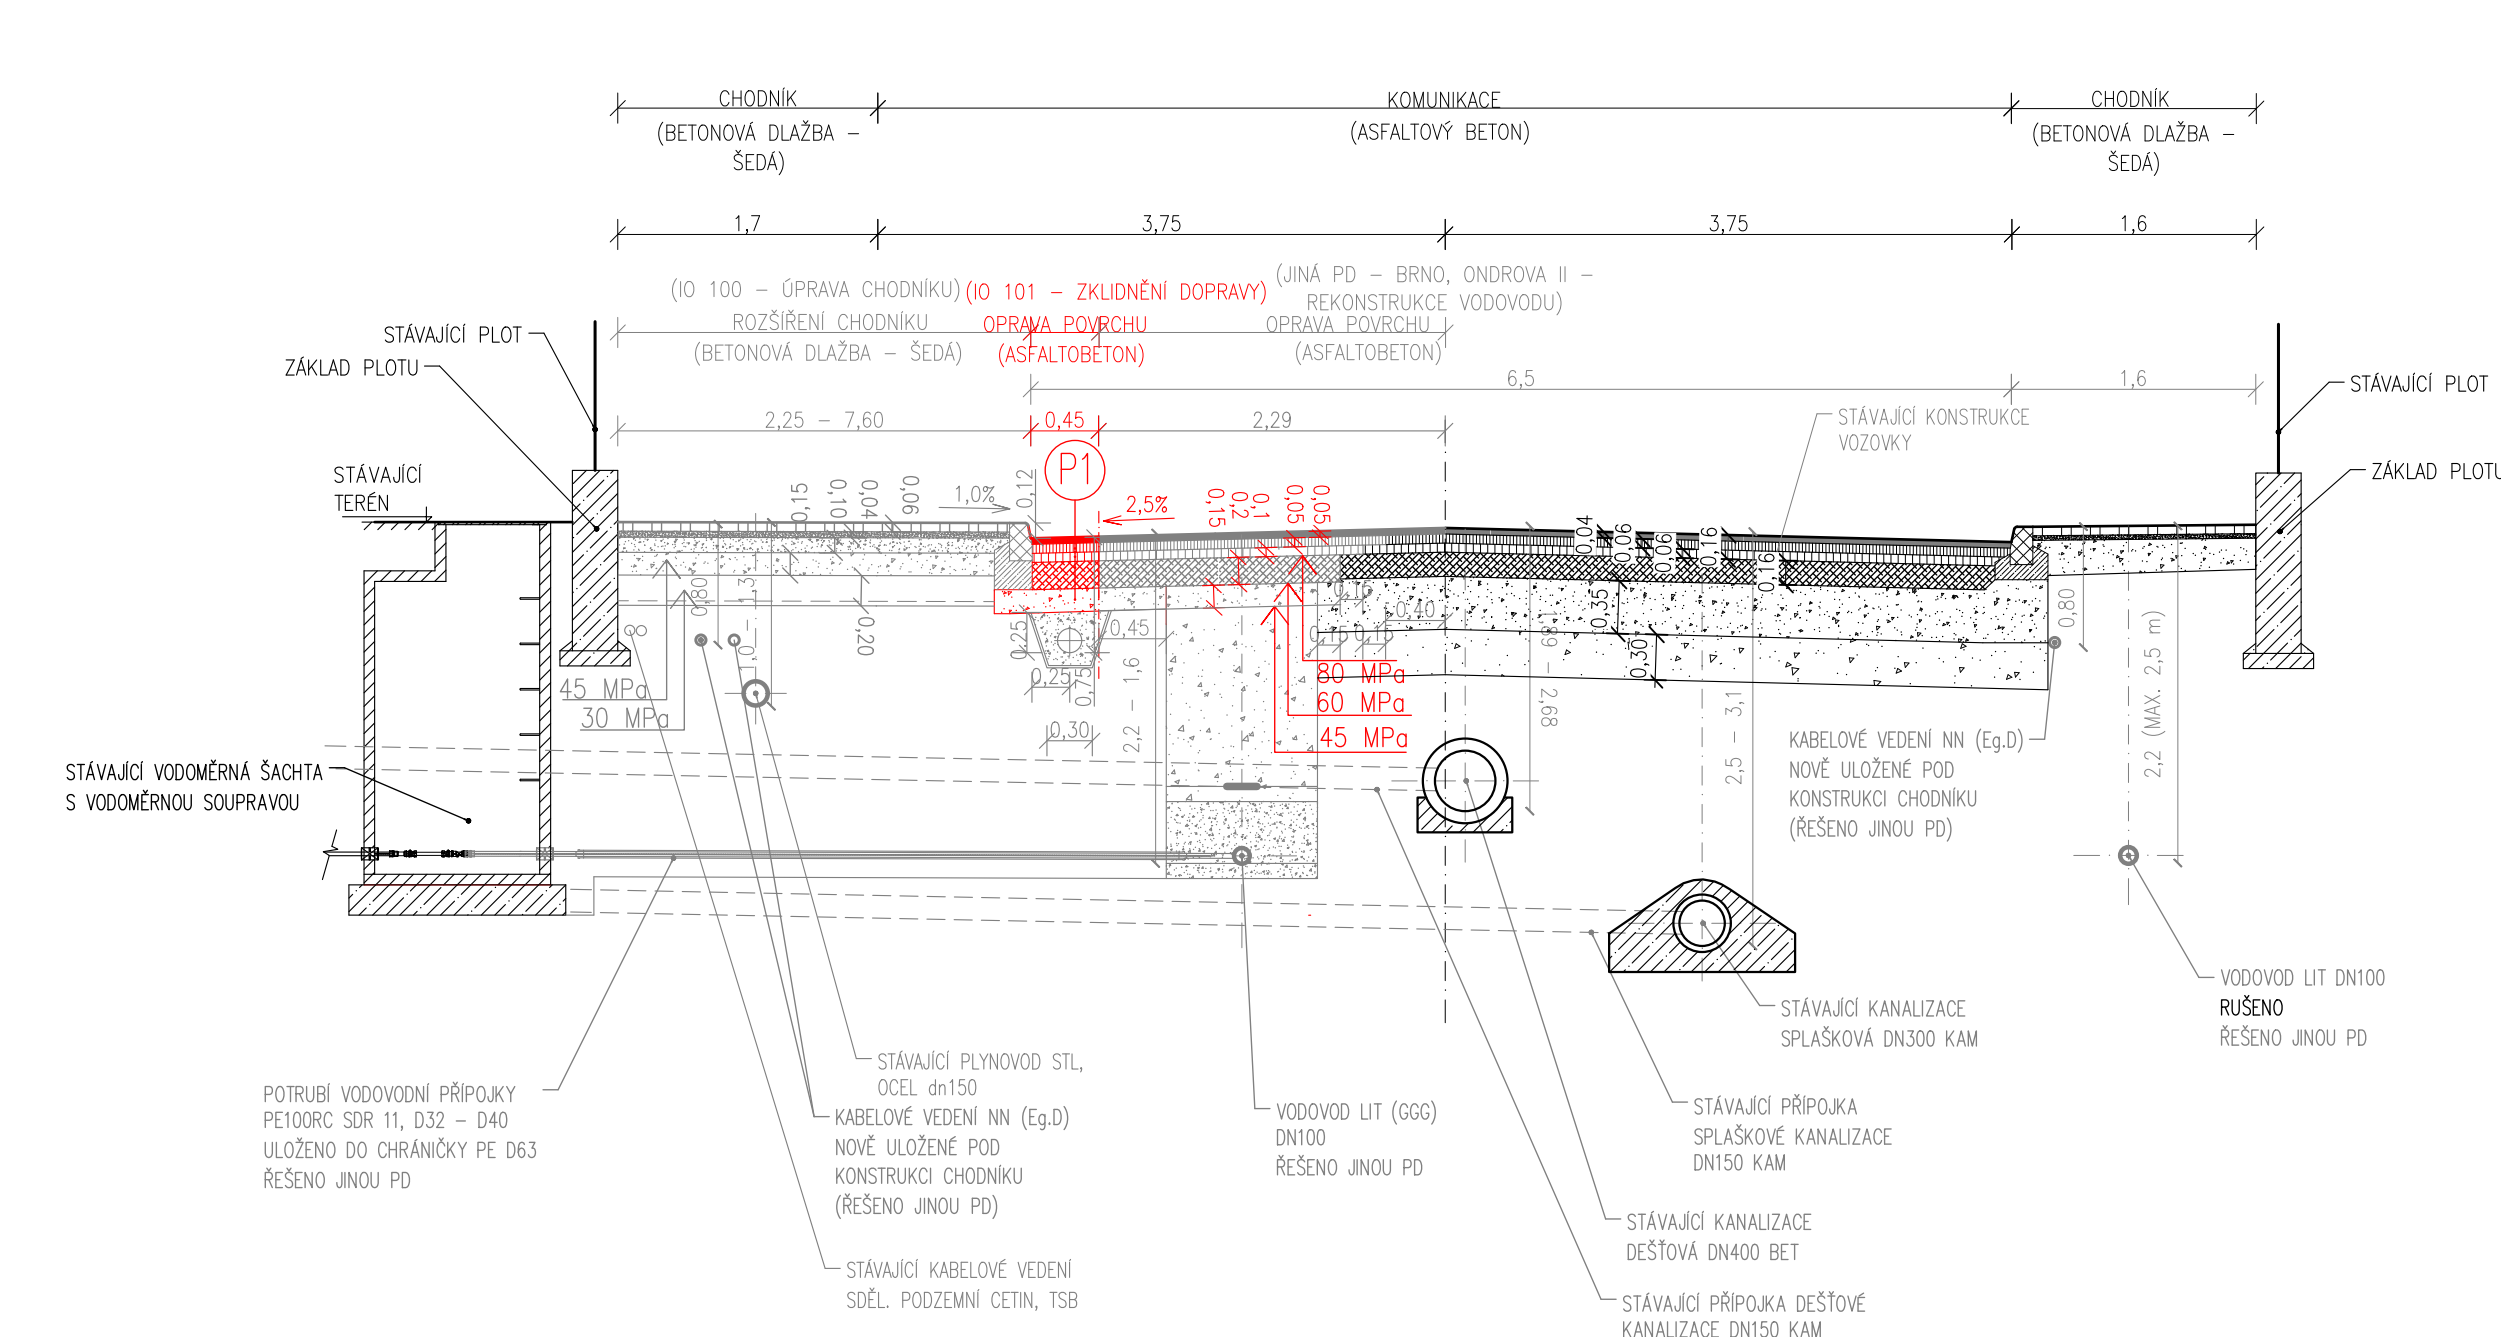


LEGENDA KONSTRUKCE POVRCHŮ


P1	POVRCH ASFALTOBETONOVÝ – KONSTRUKCE VOZOVKY PROVEDENA DLE KATALOGOVÉHO LISTU TP 170: D0–A–3–III–PIII	
	ASFALTOVÝ BETON PRO OBRUSNÉ VRSTVY – ACO 11+	ČSN EN 13108 50 mm
	POSTŘÍK SPOJOVACÍ – PS-E (0,5 kg/m ²)	ČSN 73 6129
	ASFALTOVÝ BETON PRO LOŽNÍ VRSTVY – ACL 16+	ČSN EN 13108 50 mm
	POSTŘÍK INFILTRAČNÍ – PI-E (1,0 kg/m ²)	ČSN 73 6129
	ASFALTOVÝ BETON PRO PODKLADNÍ VRSTVY – ACP 22+	ČSN EN 13108 100 mm
	SE ZESÍLENOU VRSTVOU ACP 16S o 10 mm	
	VRSTVA ZE SMĚSI STMELENÉ CEMENTEM SC – C8 / 10 (80 MPa)	ČSN EN 13108 200 mm
	ŠTERKODŘ – ŠD _A fr. 0–63 mm (60 MPa)	ČSN 73 6126 150 mm
	HUTNĚNÁ ZEMNÍ PLÁŇ (45 MPa)	
	CELKEM	550 mm

P2	KONSTRUKCE KOMUNIKACE V MÍSTĚ ZASTÁVKY AUTOBUSŮ MHD – KONSTRUKCE VOZOVKY PROVEDENA DLE NÁSLEDUJÍCÍHO SLOŽENÍ: CB I (CEMENTOBETONOVÁ DESKA C 30; – XF4, XD3 – DRÁTKOBETON VYTIŽENÁ KARI SÍŤ OKO 150/150 mm, DRÁT Ø 8 mm	220 mm
	INFILTRAČNÍ VRSTVA – NEPROPUSTNÁ FÓLIE DVOUVRSTVÁ	–
	VRSTVA ZE SMĚSI STMELENÉ CEMENTEM SC – C8 / 10 (80 MPa)	ČSN EN 13108 180 mm
	ŠTERKODŘ – ŠD _A fr. 0–63 mm (60 MPa)	ČSN 73 6126 200 mm
	HUTNĚNÁ ZEMNÍ PLÁŇ (45 MPa)	
	CELKEM	600 mm


VZOROVÝ PŘÍČNÝ ŘEZ CHODNÍKU

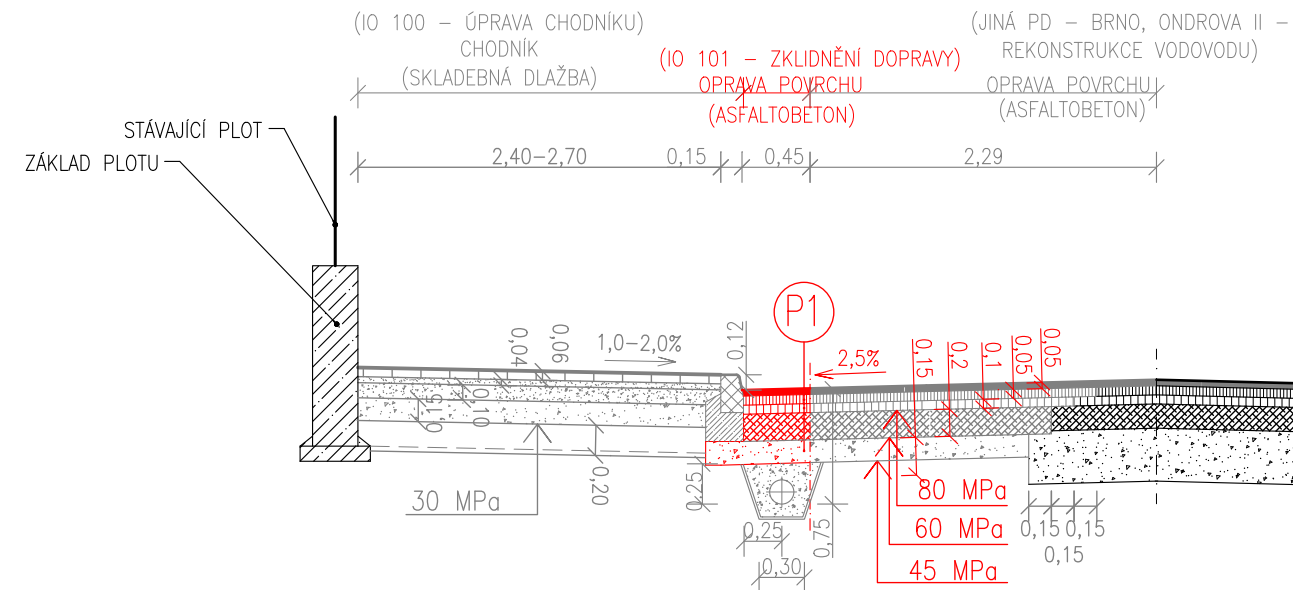


DETAIL VJEZDU K NEMOVITOSTI V PROSTORU CHODNÍKU

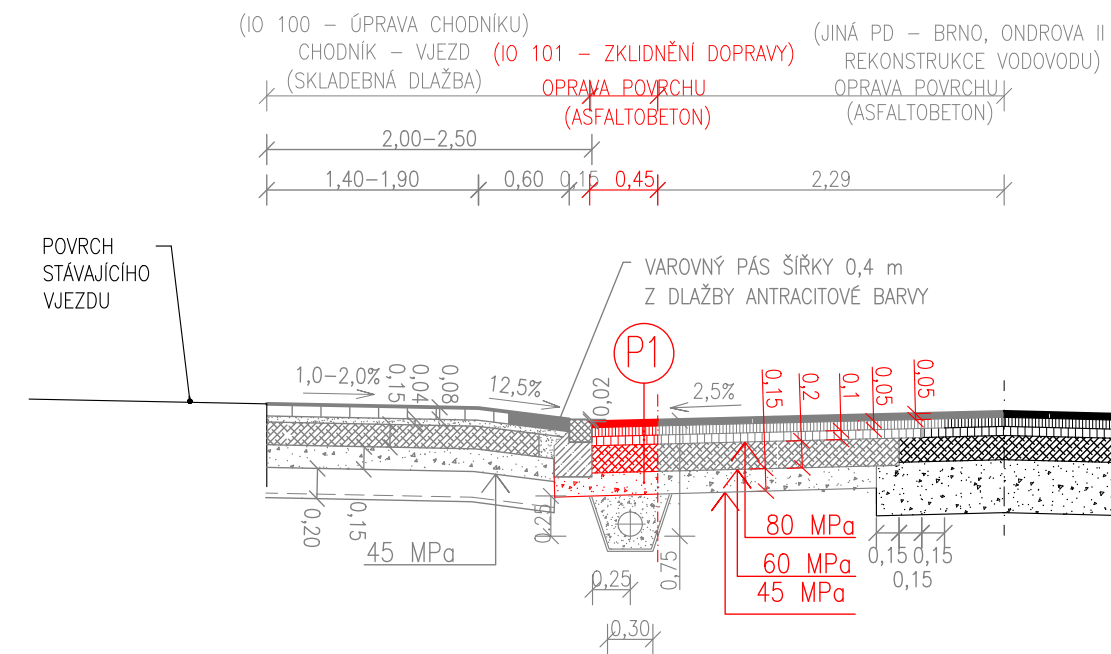


DETAIL CHODNÍKU V MÍSTĚ PŘECHODU A MÍSTA PRO PŘECHÁZENÍ

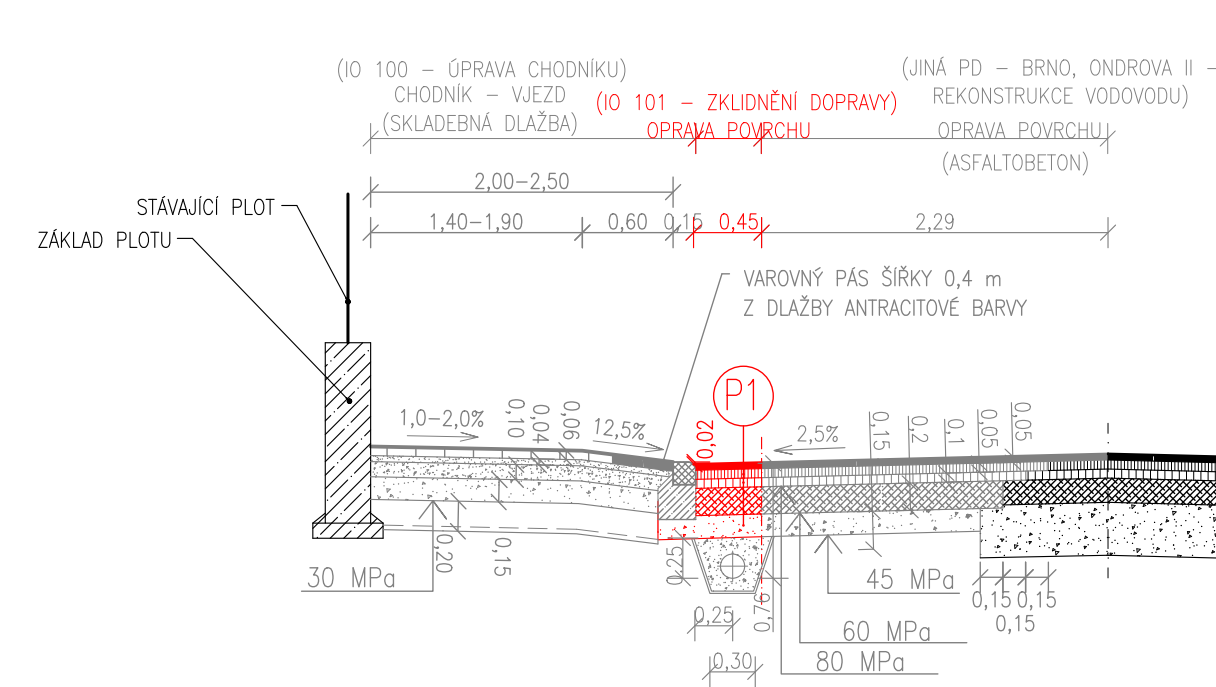

DETAIL OPRAVY POVRCHŮ V OBYTNÉ ZÓNĚ

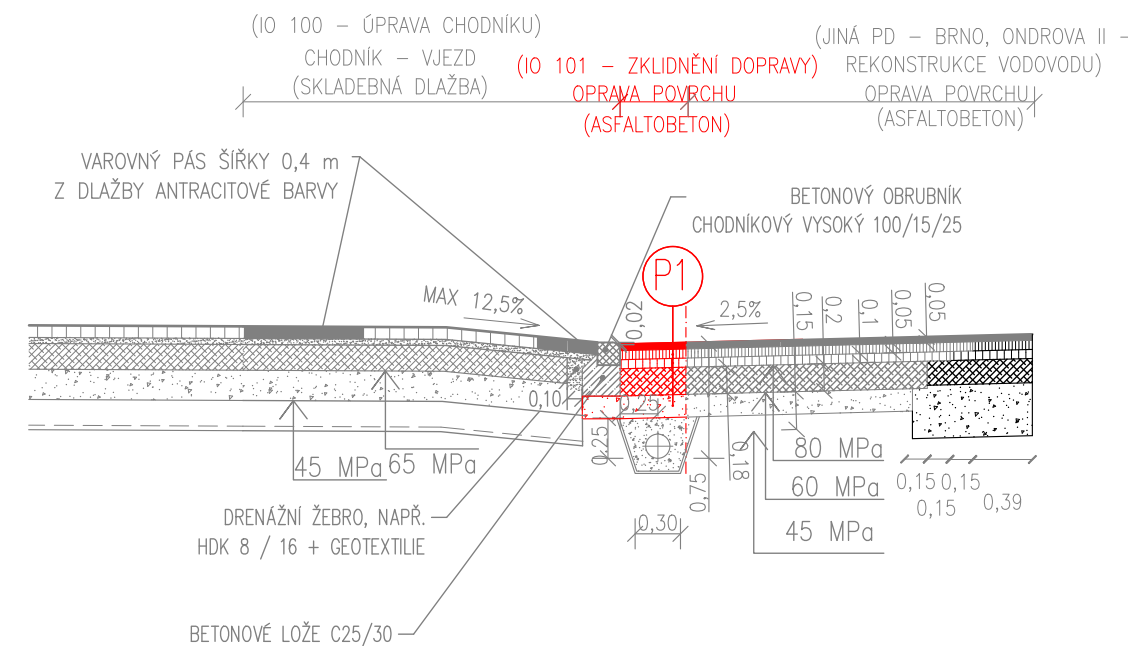

VZOROVÝ PŘÍČNÝ ŘEZ V MÍSTĚ ZASTÁVKY AUTOBUSŮ MHD

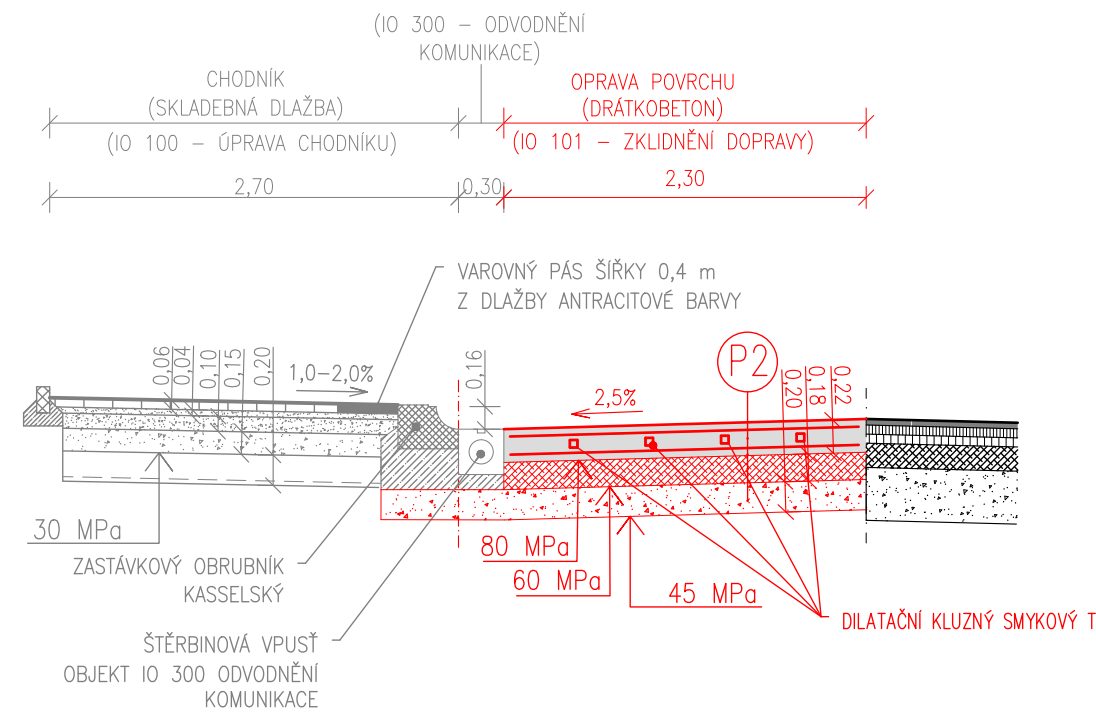

NAŘÍZ/VYPRACOVAL:	ZODPOVĚDNÝ PROJEKTANT:	VEDOUcí PROJEKTANT:	TECHNICKÁ KONTROLA:
ING. MAJER	ING. HALOUZKA	ING. HALOUZKA	ING. HALOUZKA

KRAJ:	JIHOMORAVSKÝ	KATASTR. OZEM:	KNÍNIČKY [610330]
-------	--------------	----------------	-------------------

OBJEDNATEL: Brněnské komunikace a.s.
Renesácká třída 787/1a, 639 00 Brno – Štýřice

AKCE: **ULICE ONDROVA, ZKLIDNĚNÍ DOPRAVY**

OBJEKT: **IO 101 ZKLIDNĚNÍ DOPRAVY**

VZOROVÉ PŘÍČNÉ ŘEZY



Mojmírova nám. 3105/6a, 612 00 Brno
IČ: 29262747, TEL.: 605 114 896

DATUM: 11/2024

STUPEŇ: D0SP/PDPS

FORMÁT: 5x4

MĚRITKO: 1:100
ČÍSLO PŘÍLOHY: D.2.3.